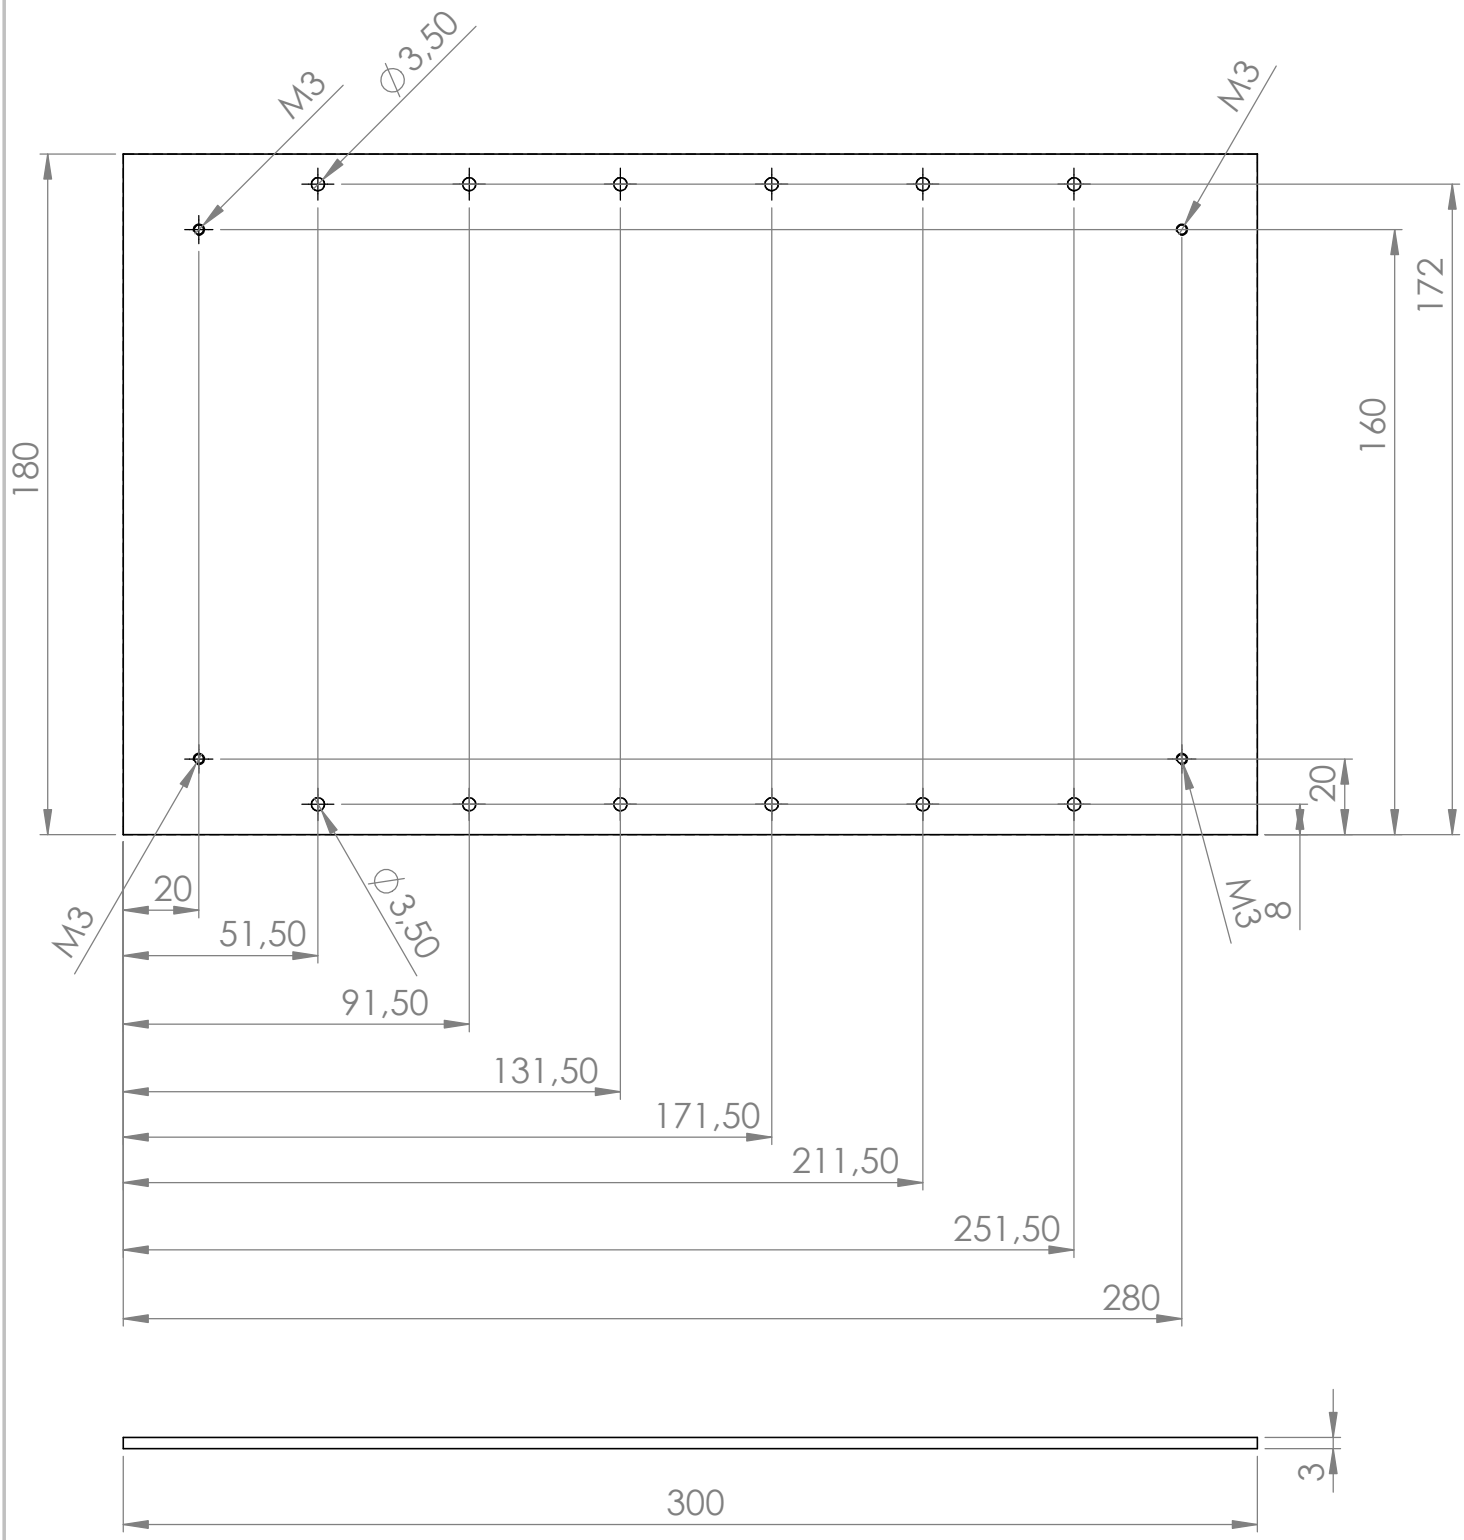

SE NON SPECIFICATO: QUOTE IN MILLIMETRI FINITURA SUPERFICIE: TOLLERANZE: LINEARE: ANGOLARE:	FINITURA: $PRPSHEET:{Fine}	SBAVATURA E INTERRUZIONE DEI BORDI NETTI	NON SCALARE IL DISEGNO / REVISIONE

	NOME	FIRMA	DATA
DISEGNATO			
VERIFICATO			
APPROVATO			
FATTO			
QUALITA'			

MATERIALE: $PRPSHEET:{Materiale}

PESO: $PRPSHEET:{Peso}

TITOLO:

P4 INCOMPLETO

NOTA: Bisogna inserire i fori relativi al Portalampada ed alla Maniglia

SCALA:1:1

FOGLIO 1 DI 1